ИНТЕРЬЕР ДИЗАЙНЫ ТӨСӨЛ · HDB BTO · СИНГАПУР

# 4 төлөвлөгөөний интерьер шийдэл

Өгөгдсөн HDB зургуудын дагуу өрөө бүрийн тавилгын байршил, хэмжээ, материал, өнгө, гэрэлтүүлэг. Бүх төлөвлөгөөнд нэг ижил хэв маяг, өнгө, материалын системийг ашигласан.

төлөвлөгөө 01

### 2-өрөө Flexi · Type 1

**40 м²**

Дотоод 38 м² + агааржуулагчийн тавиур · 1 унтлагын, 1 угаалгын

**Дэлгэрэнгүй →**

төлөвлөгөө 02

### 2-өрөө Flexi · Type 2

**49 м²**

Дотоод 46 м² · 1 унтлагын + уян хатан өрөө, 1 угаалгын

**Дэлгэрэнгүй →**

төлөвлөгөө 03

### 3-өрөө

**67 м²**

Дотоод 64 м² · 2 унтлагын, 2 угаалгын, гал тогоо + ахуйн хэсэг

**Дэлгэрэнгүй →**

төлөвлөгөө 04

### 4-өрөө

**90 м²**

Дотоод 86 м² · 3 унтлагын, 2 угаалгын, service yard

**Дэлгэрэнгүй →**

## Хэв маяг: Japandi — дулаан минимал

Японы энгийн, цэгцтэй байдал ба Скандинавын дулаан тав тухыг хослуулсан хэв маяг. Сингапурын халуун, чийглэг уур амьсгалд цайвар өнгө, байгалийн мод, ус тэсвэртэй материал, цөөн эд зүйлтэй зохион байгуулалт хамгийн тохиромжтой. Жижиг талбайтай HDB байранд орон зайг том, агаартай харагдуулна.

**1. Нэг шал, бүх өрөөнд**
Хуурай өрөөнүүдэд ижил SPC шал тасралтгүй — орон зай том харагдана.

**2. Тааз хүртэлх шүүгээ**
Суурилуулсан шүүгээг таазанд тулгаж, дээд хэсгийг улирлын хадгалалтад.

**3. Хөлтэй, хөнгөн тавилга**
Шал харагдах тусам өрөө том харагдаж, цэвэрлэгээ хялбар болно.

**4. Гурван давхар гэрэл**
Ерөнхий (тааз), ажлын (ширээ, тавцан), уур амьсгалын (шал, хана).

## Өнгөний палитр

| | | | |
|---|---|---|---|
| **Дулаан цагаан** | **Цайвар элсэн** | **Sage ногоон** | **Цайвар царс** |
| #F2EFE9 | #E6DCCB | #8C9C86 | #C9A27A |
| Үндсэн хана | Хөшиг, хивс | Онцлох хана, дээд шүүгээ | Тавилга, шал |
| **Маалинган саарал** | **Чулуун саарал** | **Цэвэр цагаан** | **Нүүрсэн хар** |
| #CFC6B8 | #BDB7AD | #FAFAF7 | #2B2D2B |
| Буйдан, даавуу | Угаалгын хавтан | Тааз, гал тогоо | Бариул, металл, гэрэл |

Харьцаа: 60% дулаан цагаан (хана, тааз) · 30% царс ба элсэн (тавилга, текстиль) · 10% sage ба хар (онцлох).

## Материалын хуваарь (бүх төлөвлөгөөнд)

| ЭЛЕМЕНТ | МАТЕРИАЛ, ҮЗҮҮЛЭЛТ | ӨНГӨ / ӨНГӨЛГӨӨ | ХААНА |
|---|---|---|---|
| **Шал** | SPC винил, 5 мм зузаан, 0.3 мм элэгдлийн давхарга, 1220×180 мм самбар, доор нь 1.5 мм IXPE дэвсгэр. Ус тэсвэртэй. | Цайвар царсны хээ, матт | Зочны, хоолны, унтлагын өрөө, хонгил |
| **Шалны хүрээ** | PVC эсвэл алюмин, 80 мм өндөр | Цагаан матт | Бүх хуурай өрөө |
| **Хана** | Усан суурьтай акрил будаг, угаагддаг, 2 давхар (~10 м²/л нэг давхарт) | Дулаан цагаан #F2EFE9, эгшелл | Бүх хуурай өрөө |
| **Онцлох хана** | Мөн адил будаг, 1 өрөөнд 1 хана | Sage #8C9C86, матт | Орны толгойн хана, ТВ-ийн ард |
| **Тааз** | Таазны будаг; зочны өрөөнд гипсэн L-хайрцаг (сонголт) далд LED-тэй | Цэвэр цагаан #FAFAF7 | Бүх өрөө |
| **Суурилуулсан шүүгээ** | 18 мм фанер их бие + HPL ламинат, зөөлөн хаагчтай нугас, гулсдаг хаалганд хөнгөн цагаан зам | Матт цагаан, царсны шпон | Хувцасны, гутлын, ТВ-ийн шүүгээ |
| **Гал тогооны шүүгээ** | Ус тэсвэртэй 18 мм фанер + HPL; доод 60 см гүн, дээд 35 см гүн | Доод: матт цагаан · Дээд: sage | Гал тогоо |
| **Тавцан** | Кварц 20 мм, доод угаалтуур суулгах нүхтэй | Цагаан / цайвар саарал | Гал тогоо, угаалгын тавцан |
| **Гал тогооны хана** | Метро хавтан 75×300 мм эсвэл 6 мм шил | Цагаан гялгар / sage шил | Тавцангаас дээш 60 см |
| **Угаалгын өрөө** | Шал: 300×300 порцелан, гулсахгүй R11 · Хана: 300×600 порцелан | Чулуун саарал #BDB7AD, матт | Угаалгын өрөө |
| **Хаалга** | Ламинат хаалга, хар матт бариул; угаалгын өрөөнд эвхэгддэг/ус тэсвэртэй | Цагаан эсвэл царсны шпон | Өрөөнүүд |
| **Хөшиг** | Давхар зам: нимгэн тюль + блэкаут (унтлагын өрөөнд), маалинга-полиэстер | Цайвар элсэн #E6DCCB | Бүх цонх |
| **Металл, бариул** | Нунтаг будгаар бүрсэн хөнгөн цагаан / ган | Нүүрсэн хар #2B2D2B | Бариул, гэрлийн хүрээ, тавиур |

## Хөдөлгөөний чөлөөт зай

| ХААНА | ХАМГИЙН БАГА |
|---|---|
| Үндсэн явах зам, коридор | `90 см` |
| Орны хажуу (ор засах) | `60 см` |
| Шүүгээний урд — эргэдэг хаалга | `90 см` |
| Шүүгээний урд — гулсдаг хаалга | `70 см` |
| Хоолны сандлын ард | `75 см (явах бол 90)` |
| Буйдан ба кофе ширээ | `40–45 см` |
| Гал тогооны тавцангийн урд | `100–120 см` |
| Хөргөгчийн хаалга нээх | `90 см` |
| Жорлонгийн урд | `60 см` |
| Ажлын ширээний сандал татах | `80 см` |

## Стандарт өндөр, хэмжээ

| ЭЛЕМЕНТ | ХЭМЖЭЭ |
|---|---|
| Гал тогооны тавцан | `85–90 см` |
| Дээд шүүгээний доод ирмэг | `шалнаас 145–150 см` |
| Хоолны / ажлын ширээ | `75 см (сандал 45)` |
| Угаалтуурын тавцан | `80–85 см` |
| Толины төв | `150–160 см` |
| ТВ дэлгэцийн төв | `шалнаас 100–110 см` |
| ТВ үзэх зай | `≈ диагональ × 1.5` |
| Залгуур / тавцан дээрх залгуур | `30 см / 110 см` |
| Хөшигний мод | `цонхноос 15–20 см дээш` |
| Матрас: Single / S.Single / Queen / King | `91 / 107 / 152 / 183 × 190` |

## Гэрэлтүүлгийн стандарт

| ӨРӨӨ | ӨНГӨНИЙ ТЕМПЕРАТУР | ШИЙДЭЛ |
|---|---|---|
| **Зочны өрөө** | `3000K` | 10–12W LED downlight 1.2–1.5 м зайтай, бүдгэрүүлэгчтэй (dimmer); ТВ-ийн ард LED тууз; буйдангийн хажууд шалны гэрэл |
| **Хоолны хэсэг** | `2700–3000K` | Ширээний төв дээр унжлагат гэрэл, ширээнээс 75–85 см өндөрт |
| **Унтлагын өрөө** | `2700–3000K` | Таазны гэрэл + орны хажуугийн ханын гэрэл (шалнаас ~120 см), шүүгээний дотор хөдөлгөөний мэдрэгчтэй LED |
| **Гал тогоо** | `4000K` | Таазны downlight + дээд шүүгээний доор LED тууз (тавцан гэрэлтүүлэг) |
| **Угаалгын өрөө** | `4000K` | Чийгт тэсвэртэй IP44+ гэрэл, LED толь; агааржуулах сэнс |
| **Ажлын булан** | `4000K` | Ширээний чийдэн + тавиурын доорх LED |

## HDB-ийн дүрэм — заавал шалгах

- **Хамгаалах өрөө (Household shelter):** хана, шал, таазыг цоолох, өрөмдөх, юм бэхлэх хориотой. Зөвхөн чөлөөтэй зогсох тавиур тавина; хаалгыг хааж болохгүй.

## Хэмжээний тухай тайлбар

- Өрөөний хэмжээг HDB-ийн зургийн харьцаа ба өгөгдсөн нийт талбайгаас (40 / 49 / 67 / 90 м²) тооцсон **ойролцоо** утга, алдаа ±10–15 см.

ТӨЛӨВЛӨГӨӨ 01 · 2-ӨРӨӨ FLEXI

# 2-өрөө Flexi · Type 1

1–2 хүнд зориулсан нягт, цэгцтэй шийдэл. Зочны болон хоолны хэсгийг нэг орон зайд нэгтгэж, унтлагын өрөөнд суурилуулсан шүүгээ, орны доорх хадгалалтаар зай хэмнэнэ.

Нийт талбай
**40 м²**

Дотоод талбай
**38 м²**

Өрөө
**1 унтлагын · 1 угаалгын**

Хэнд
**Ганц бие, хос, ахмад**

## Тавилгын байршлын зураг

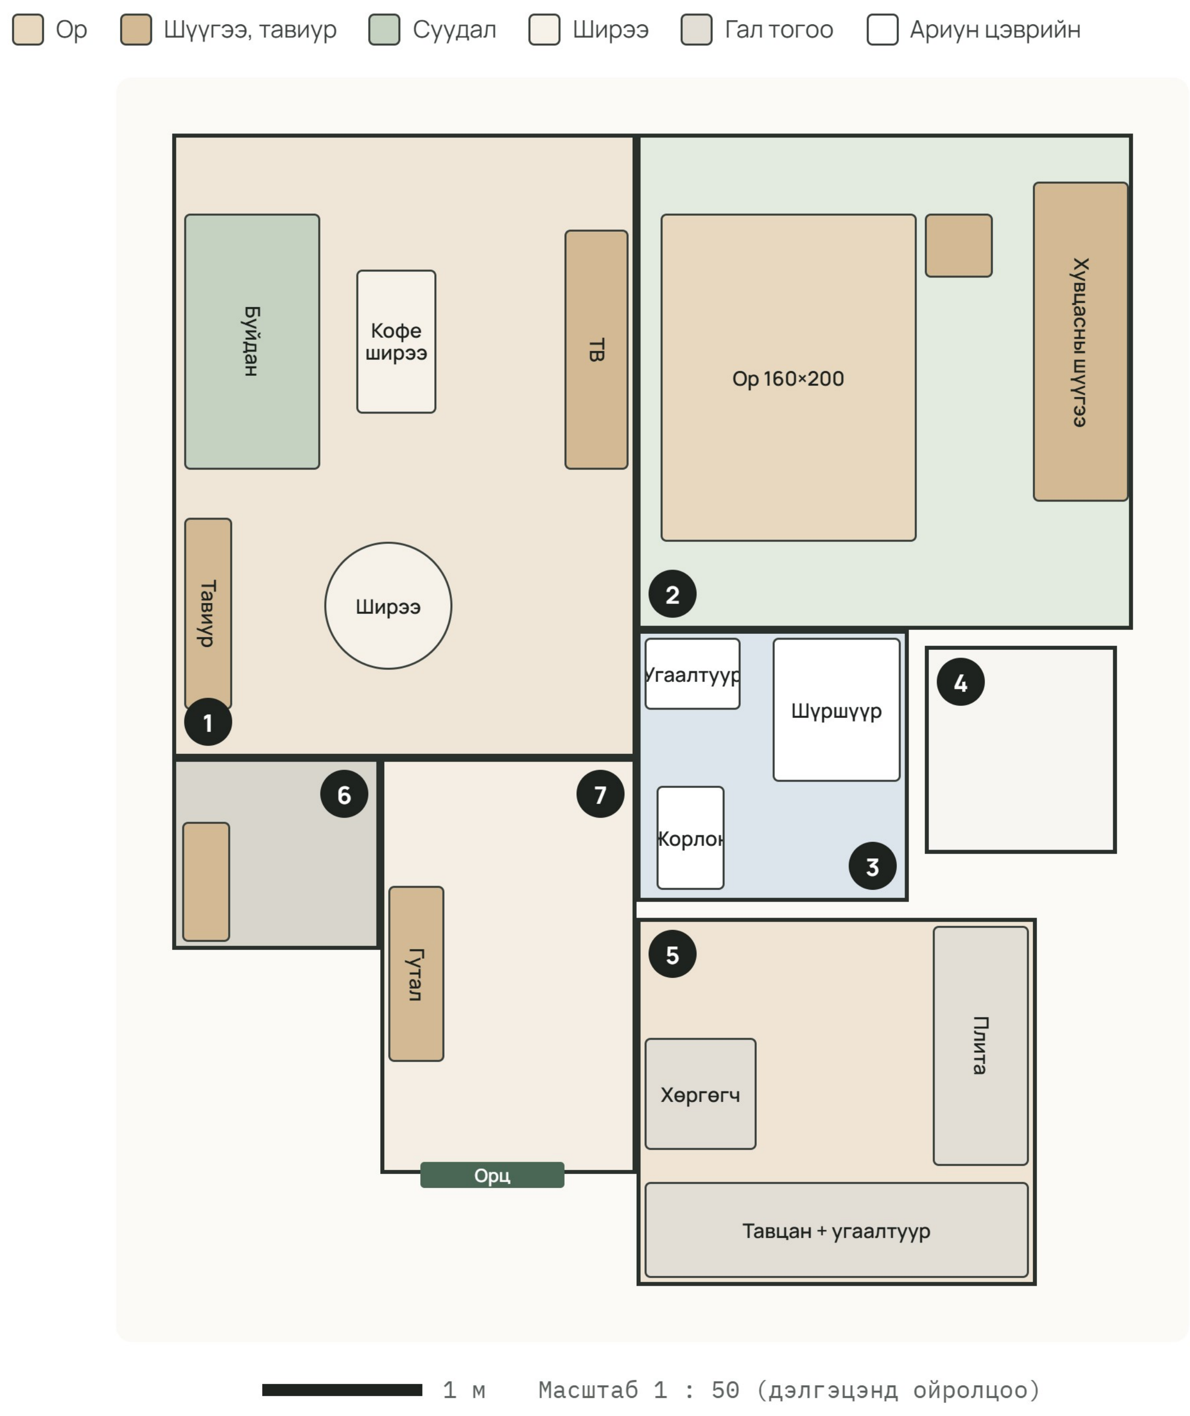

## Өрөөний хэмжээ (ойролцоо)

| № | ӨРӨӨ | ХЭМЖЭЭ, М | ТАЛБАЙ |
|---|---|---|---|
| 1 | Зочны / хоолны өрөө | 2.9 × 3.9 | 11.3 м² |
| 2 | Унтлагын өрөө | 3.1 × 3.1 | 9.6 м² |
| 3 | Угаалгын өрөө | 1.7 × 1.7 | 2.9 м² |
| 4 | Агааржуулагчийн тавиур | 1.2 × 1.3 | 1.6 м² |
| 5 | Гал тогоо | 2.5 × 2.3 | 5.8 м² |
| 6 | Хамгаалах өрөө (Shelter) | 1.3 × 1.2 | 1.6 м² |
| 7 | Орох хонгил | 1.6 × 2.6 | 4.2 м² |

**Шалны сонголт**

Энэ төрөл анхнаасаа зочны, хоолны, унтлагын өрөөний шалны өнгөлгөөгүй (default) эсвэл өнгөлгөөтэй хувилбартай. Өнгөлгөөгүй авсан бол SPC винил шал тавина: ~28 м² (10% нөөцтэй).

**Гол санаа**

Зочны өрөөнд буйдан зүүн хананд, ТВ баруун хананд — дунд нь 90 см чөлөөт зам. Хоолны дугуй ширээ булан эзлэхгүй, хонгил руу чөлөөтэй гарна.

# Өрөө тус бүрийн тавилга, хэмжээ, материал

### 01 Зочны / хоолны өрөө

2.9 × 3.9 м

| ТАВИЛГА | Ө × Г × Ө, СМ | МАТЕРИАЛ / ӨНГӨ |
|---|---|---|
| Буйдан, 2 хүний | 160×85×80 | Маалинган бүрээс #CFC6B8, царсан хөл |
| Кофе ширээ | 90×50×40 | Цайвар царс, бөөрөнхий өнцөг |
| ТВ тавиур (дүүжин) | 150×40×40 | Царсны шпон + цагаан; шалнаас 20 см дээш |
| ТВ | 43" | Үзэх зай ~1.6 м; дэлгэцийн төв 100 см |
| Хоолны ширээ, дугуй | Ø80×75 | Царс; 2–3 сандал 45×50×80 |
| Номын тавиур | 120×30×180 | Царс + хар металл |
| Хивс | 160×230 | Нэхмэл, цайвар элсэн #E6DCCB |
| Гэрэл | 4 + 1 | Downlight 3000K ×4, шалны гэрэл ×1, хоолны унжлагат гэрэл |

Онцлох хана: ТВ-ийн ард sage #8C9C86. Буйдан ба ширээний хооронд 45 см.

### 02 Унтлагын өрөө

3.1 × 3.1 м

| ТАВИЛГА | Ө × Г × Ө, СМ | МАТЕРИАЛ / ӨНГӨ |
|---|---|---|
| Ор, Queen (хүрээ) | 160×205×100 | Матрас 152×190; доороо шургуулгатай, даавуун толгой |
| Шөнийн ширээ | 42×40×50 | Царс, 1 шургуулга |
| Хувцасны шүүгээ | 200×60×240 | Гулсдаг хаалга, матт цагаан, хар бариул |
| Ханын гэрэл | 1 ш | 2700K, шалнаас 120 см, орны хажууд |
| Хөшиг | цонх +30 | Блэкаут + тюль, давхар зам |
| Таазны гэрэл | 1–2 ш | Нимгэн LED панел, 3000K |

Ор зүүн хананд тулж, баруун талд 80 см зам үлдэнэ. Гулсдаг хаалга эргэдэг хаалганаас 20 см зай хэмнэнэ. Орны толгойн хана sage.

### 05 Гал тогоо

2.5 × 2.3 м

| ЭЛЕМЕНТ | Ө × Г × Ө, СМ | МАТЕРИАЛ / ӨНГӨ |
|---|---|---|
| Доод шүүгээ, L хэлбэр | 240 + 150 × 60 × 88 | Фанер + HPL, матт цагаан |
| Дээд шүүгээ | 240×35×70 | Sage матт; доод ирмэг шалнаас 150 см |
| Тавцан | 20 мм | Кварц, цагаан |
| Угаалтуур | 60×45 | Зэвэрдэггүй ган, нэг тасалгаа |
| Плита + сорогч | 60 см | Индукц 2 зуух; сорогч 65–75 см дээр |
| Хөргөгч | 60×70×180 | 2 хаалгатай |
| Угаалгын машин | 60×60×85 | Урдаас ачдаг, тавцангийн доор |

Хөргөгч → угаалтуур → плита ажлын гурвалжин 4–6 м. Дээд шүүгээний доор LED тууз 4000K.

### 03 Угаалгын өрөө

1.7 × 1.7 м

| ЭЛЕМЕНТ | Ө × Г × Ө, СМ | МАТЕРИАЛ / ӨНГӨ |
|---|---|---|
| Угаалтуурын шүүгээ (дүүжин) | 60×45×50 | Ус тэсвэртэй, цагаан; тавцан 85 см өндөрт |
| Толин шүүгээ | 60×12×70 | LED хүрээтэй, 4000K |
| Жорлон | 38×65 | Цагаан, ханын ойролцоо |
| Шүршүүр | 80×90 | 8 мм тунгалаг шилэн хаалт, урт ус зайлуулагч |
| Хавтан | 300×300 / 300×600 | Чулуун саарал #BDB7AD, гулсахгүй |
| Дагалдах | – | Алчуурын мод, дэгээ — хар матт |

Ахмад хүнд: жорлон, шүршүүрийн хажууд бариул (grab bar) суулгахыг зөвлөнө.

### 06 · 07 Орох хонгил ба Shelter

| ЭЛЕМЕНТ | Ө × Г × Ө, СМ | МАТЕРИАЛ / ӨНГӨ |
|---|---|---|
| Гутлын шүүгээ (нарийн) | 110×35×120 | Царс + цагаан; дээд тал түлхүүрийн тавиур |
| Бүтэн биеийн толь | 50×170 | Хар нарийн хүрээ, ханан дээр |
| Shelter тавиур | 75×30×180 | Чөлөөтэй зогсох металл; ханад бэхлэхгүй |
| Гэрэл | 2 ш | Downlight 3000K |

### Σ Тоо хэмжээ (ойролцоо)

| МАТЕРИАЛ | ТОО | ТАЙЛБАР |
|---|---|---|
| SPC шал | ~28 м² | Өрөө 1, 2, 7 |
| Ханын будаг | ~20 л | ~95 м² хана, 2 давхар |
| Sage будаг | ~4 л | 2 онцлох хана |
| Downlight | ~9 ш | Зочны 4, унтлагын 2, хонгил 2, гал тогоо 1 |
| Залгуур (нэмэлт) | ~6 ш | ТВ 2, орны хажуу 2, гал тогооны тавцан 2 |

---

Өрөөний хэмжээ нь HDB-ийн зургийн харьцаа ба 38 м² дотоод талбайгаас тооцсон ойролцоо утга (±10–15 см). Суурилуулсан тавилга захиалахаас өмнө газар дээр нь хэмжинэ. Материал, өнгөний дэлгэрэнгүйг «Ерөнхий» самбараас үзнэ үү.

ТӨЛӨВЛӨГӨӨ 02 · 2-ӨРӨӨ FLEXI

# 2-өрөө Flexi · Type 2

Type 1-ээс 9 м$^2$ том, унтлагын өрөөний хажууд уян хатан орон зайтай. Үүнийг ажлын булан болгож, шаардлагатай үед зочны ор эсвэл хоолны хэсэг болгон хувиргах боломжтой.

| Нийт талбай | Дотоод талбай | Өрөө | Хэнд |
|---|---|---|---|
| **49 м$^2$** | **46 м$^2$** | **1 унтлагын + Flexi зай** | **Хос, гэрээс ажилладаг** |

## Тавилгын байршлын зураг

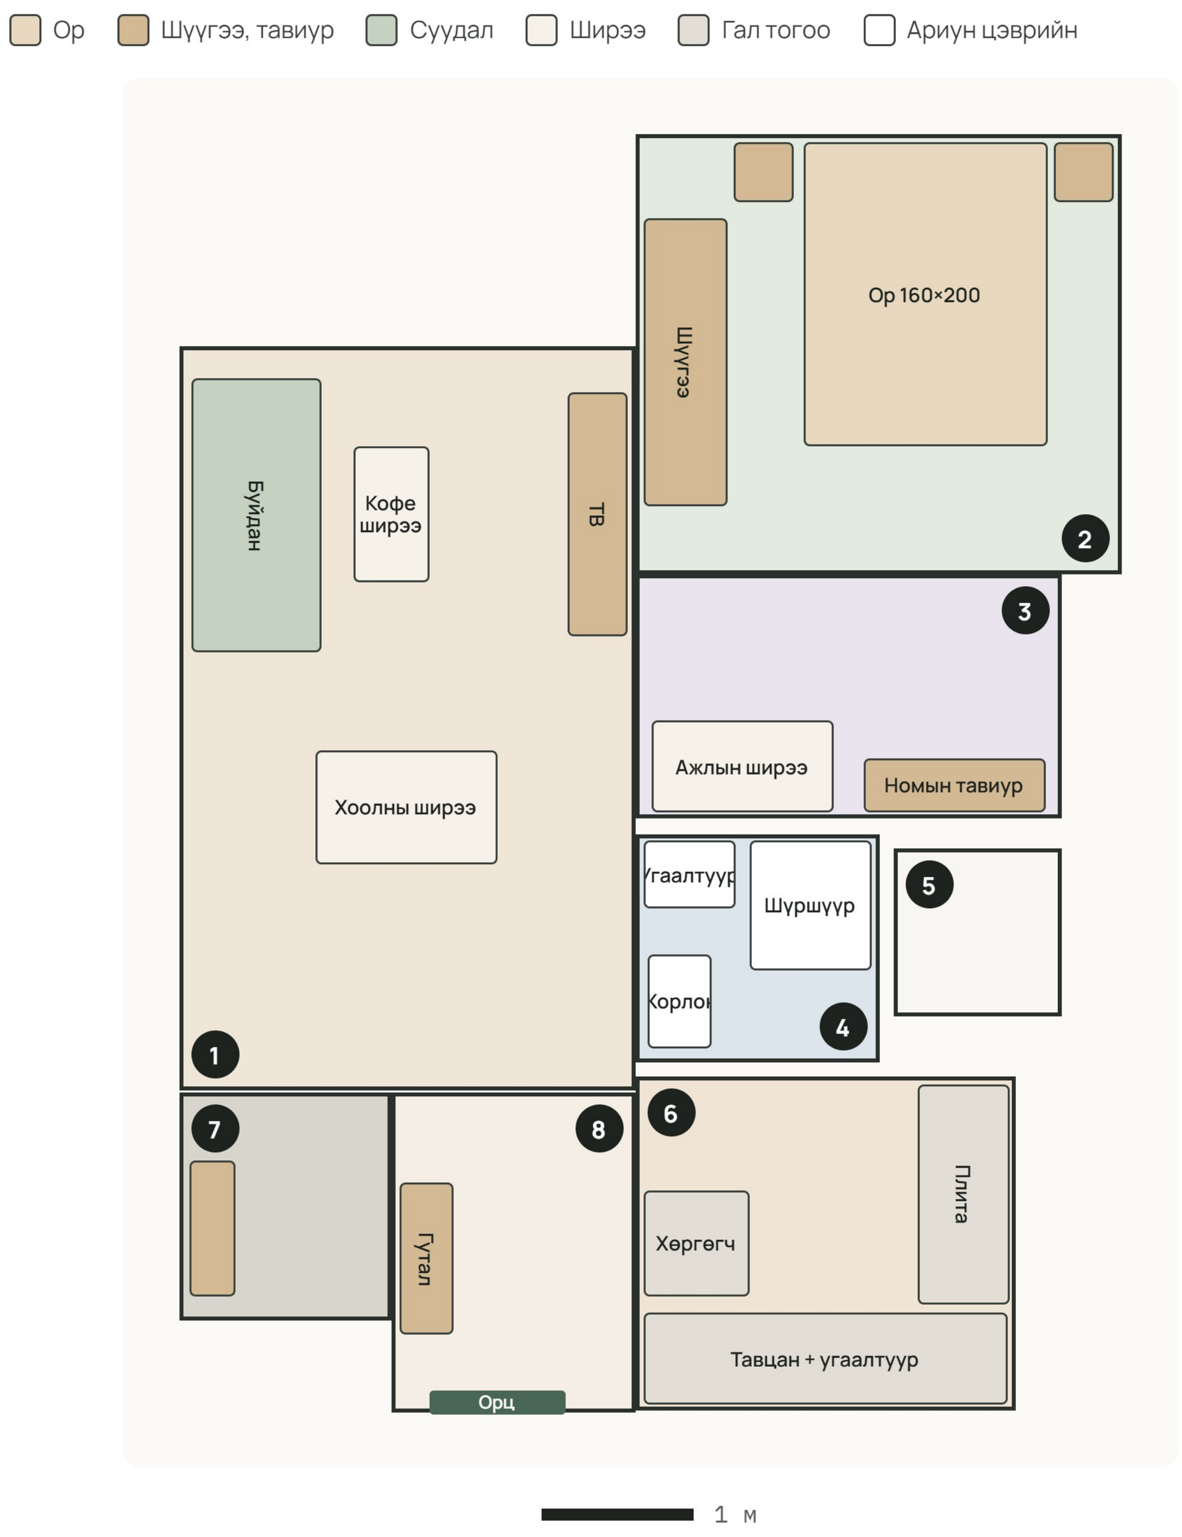

## Өрөөний хэмжээ (ойролцоо)

| № | ӨРӨӨ | ХЭМЖЭЭ, М | ТАЛБАЙ |
|---|---|---|---|
| 1 | Зочны / хоолны өрөө | 3.0 × 4.9 | 14.7 м$^2$ |
| 2 | Унтлагын өрөө | 3.2 × 2.9 | 9.3 м$^2$ |
| 3 | Уян хатан орон зай (Flexi) | 2.8 × 1.6 | 4.5 м$^2$ |
| 4 | Угаалгын өрөө | 1.6 × 1.5 | 2.4 м$^2$ |
| 5 | Агааржуулагчийн тавиур | 1.1 × 1.1 | 1.2 м$^2$ |
| 6 | Гал тогоо | 2.5 × 2.2 | 5.5 м$^2$ |
| 7 | Хамгаалах өрөө (Shelter) | 1.4 × 1.5 | 2.1 м$^2$ |
| 8 | Орох хонгил | 1.6 × 2.1 | 3.4 м$^2$ |

### Flexi орон зайн 3 хувилбар

**A. Ажлын булан** (зурагт) — ширээ 120×60 + тавиур. **B. Зочны ор** — 90×190 daybed, доороо шургуулгатай. **C. Хоолны хэсэг** — 4 хүний ширээ, зочны өрөөнд илүү зай гаргана.

### Хаалганы сонголт

Flexi зайг унтлагын өрөөнөөс тусгаарлахад HDB-ийн сонголтот ламинат uPVC эвхэгддэг хаалга (богино хугацааны түрээсийн хувилбар) эсвэл 2 хавтастай гулсдаг шилэн хаалга.

## Өрөө тус бүрийн тавилга, хэмжээ, материал

### 01 Зочны / хоолны өрөө

3.0 × 4.9 м

| ТАВИЛГА | Ө × Г × Ө, СМ | МАТЕРИАЛ / ӨНГӨ |
|---|---|---|
| Буйдан, 2.5 хүний | 180×85×80 | Маалинган бүрээс #CFC6B8, царсан хөл |
| Кофе ширээ | 90×50×40 | Цайвар царс |
| ТВ тавиур (дүүжин) | 160×40×40 | Царсны шпон + цагаан |
| ТВ | 43–50" | Үзэх зай ~1.75 м; төв нь 100 см өндөрт |
| Хоолны ширээ | 120×75×75 | Царс; 4 сандал 45×50×80 |
| Хоолны унжлагат гэрэл | Ø40 | Цайвар даавуу/цаас, ширээнээс 80 см дээр |
| Хивс | 160×230 | Цайвар элсэн #E6DCCB |
| Гэрэл | 5 + 1 | Downlight 3000K ×5, шалны гэрэл ×1 |

Зочны (дээд) ба хоолны (доод) хэсгийг хивсээр тусгаарлана. ТВ-ийн ард sage онцлох хана.

### 02 Унтлагын өрөө

3.2 × 2.9 м

| ТАВИЛГА | Ө × Г × Ө, СМ | МАТЕРИАЛ / ӨНГӨ |
|---|---|---|
| Ор, Queen (хүрээ) | 160×200×100 | Матрас 152×190; доороо шургуулгатай |
| Шөнийн ширээ ×2 | 40×40×50 | Царс; ханын гэрэл 2700K дээр нь |
| Хувцасны шүүгээ | 190×55×240 | Гулсдаг хаалга (заавал), матт цагаан |
| Хөшиг | цонх +30 | Блэкаут + тюль |
| Таазны гэрэл | 1 ш | LED панел 3000K |

Өрөө 2.9 м гүн тул орыг дээд хананд тулгаж, хөлийн талд 85 см зам гаргана. Шүүгээ ба орны хооронд 50 см — эргэдэг хаалга тохирохгүй.

### 03 Уян хатан орон зай (Flexi)

2.8 × 1.6 м

| ТАВИЛГА | Ө × Г × Ө, СМ | МАТЕРИАЛ / ӨНГӨ |
|---|---|---|
| Ажлын ширээ | 120×60×75 | Царс, кабель нуух нүхтэй |
| Ажлын сандал | 60×60×95 | Эргономик, саарал тор |
| Номын тавиур | 120×35×180 | Царс + хар металл |
| Ханын тавиур | 120×25 | Ширээнээс 45 см дээр, доор нь LED |
| Ширээний чийдэн | – | 4000K, хар матт |
| Эвхэгддэг хаалга | ≈ 160×210 | uPVC ламинат, цагаан (сонголт) |

Ширээ дээр 2, доор 1 залгуур + интернэт порт гаргана.

### 06 Гал тогоо

2.5 × 2.2 м

| ЭЛЕМЕНТ | Ө × Г × Ө, СМ | МАТЕРИАЛ / ӨНГӨ |
|---|---|---|
| Доод шүүгээ, L хэлбэр | 240 + 145 × 60 × 88 | Фанер + HPL, матт цагаан |
| Дээд шүүгээ | 240×35×70 | Sage матт; доод ирмэг 150 см |
| Тавцан | 20 мм | Кварц, цагаан |
| Угаалтуур | 60×45 | Зэвэрдэггүй ган |
| Плита + сорогч | 60 см | Индукц 2 зуух |
| Хөргөгч | 60×70×180 | 2 хаалгатай |
| Угаалгын машин | 60×60×85 | Тавцангийн доор |

### 04 Угаалгын өрөө

1.6 × 1.5 м

| ЭЛЕМЕНТ | Ө × Г × Ө, СМ | МАТЕРИАЛ / ӨНГӨ |
|---|---|---|
| Угаалтуурын шүүгээ | 60×45×50 | Дүүжин, цагаан; тавцан 85 см |
| Толин шүүгээ | 60×12×70 | LED, 4000K |
| Жорлон | 38×62 | Цагаан |
| Шүршүүр | 80×85 | 8 мм шилэн хаалт |
| Хавтан | 300×300 / 300×600 | Чулуун саарал #BDB7AD |

### 07 · 08 Орох хонгил ба Shelter

| ЭЛЕМЕНТ | Ө × Г × Ө, СМ | МАТЕРИАЛ / ӨНГӨ |
|---|---|---|
| Гутлын шүүгээ | 100×35×120 | Царс + цагаан |
| Ханын дэгээ / толь | 60×5 / 50×170 | Хар матт |
| Shelter тавиур | 90×30×180 | Чөлөөтэй зогсох; ханад бэхлэхгүй |
| Гэрэл | 2 ш | Downlight 3000K |

### Σ Тоо хэмжээ (ойролцоо)

| МАТЕРИАЛ | ТОО | ТАЙЛБАР |
|---|---|---|
| SPC шал | ~35 м$^2$ | Өрөө 1, 2, 3, 8 — 10% нөөцтэй (шалны өнгөлгөөгүй хувилбар авсан бол) |
| Ханын будаг | ~22 л | ~110 м$^2$ хана, 2 давхар |
| Sage будаг | ~4 л | ТВ-ийн ард, орны толгойн хана |
| Downlight | ~11 ш | Зочны/хоолны 5, унтлагын 1 панел, Flexi 2, хонгил 2, гал тогоо 1 |
| Залгуур (нэмэлт) | ~8 ш | ТВ 2, орны хажуу 2, ажлын ширээ 2, тавцан 2 |

---

Өрөөний хэмжээ нь HDB-ийн зургийн харьцаа ба 46 м$^2$ дотоод талбайгаас тооцсон ойролцоо утга (±10–15 см). Суурилуулсан тавилга захиалахаас өмнө газар дээр нь хэмжинэ.

ТӨЛӨВЛӨГӨӨ 03 · 3-ӨРӨӨ

# 3-өрөө орон сууц

Залуу гэр бүл эсвэл 1 хүүхэдтэй айлд. Мастер өрөө өөрийн угаалгын өрөөтэй, 2 дахь өрөө хүүхдийн эсвэл ажлын өрөө. Гал тогоо ба ахуйн хэсгийг (utility) нэгтгэсэн — тасархай шугамаар хуваалт хийж болно.

| Нийт талбай | Дотоод талбай | Өрөө | Хэнд |
|---|---|---|---|
| **67 м²** | **64 м²** | **2 унтлагын · 2 угаалгын** | **2–3 хүнтэй гэр бүл** |

## Тавилгын байршлын зураг

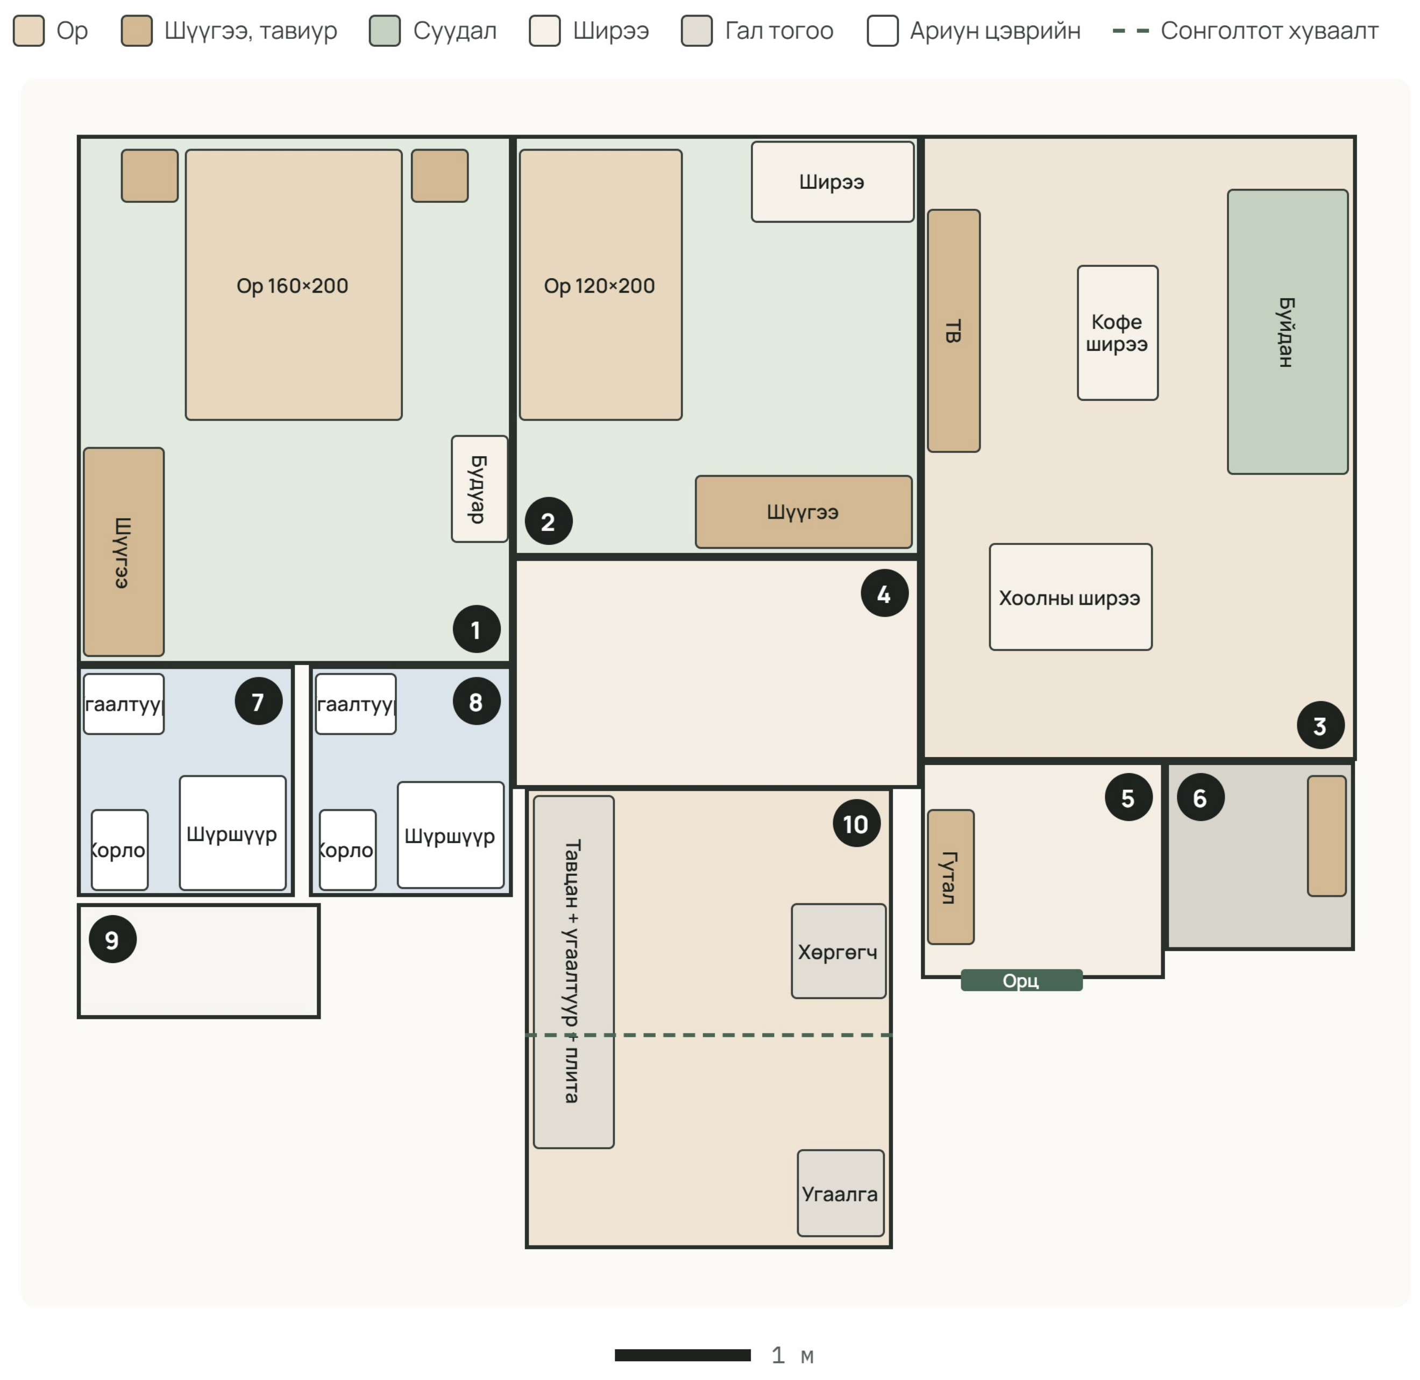

## Өрөөний хэмжээ (ойролцоо)

| № | Өрөө | Хэмжээ, м | Талбай |
|---|---|---|---|
| 1 | Мастер унтлагын | 3.2 × 3.9 | 12.5 м² |
| 2 | Унтлагын өрөө 2 | 3.0 × 3.1 | 9.3 м² |
| 3 | Зочны / хоолны | 3.2 × 4.6 | 14.7 м² |
| 4 | Хонгил | 3.0 × 1.7 | 5.1 м² |
| 5 | Орох хэсэг | 1.8 × 1.6 | 2.9 м² |
| 6 | Shelter | 1.4 × 1.4 | 2.0 м² |
| 7 | Мастер угаалгын | 1.6 × 1.7 | 2.7 м² |
| 8 | Нийтийн угаалгын | 1.5 × 1.7 | 2.6 м² |
| 9 | Агааржуулагчийн тавиур | 1.8 × 0.85 | 1.5 м² |
| 10 | Гал тогоо / ахуйн | 2.7 × 3.4 | 9.2 м² |

**Гал тогооны хуваалт**

HDB гал тогоо ба ахуйн хэсгийг нэгтгэсэн. Тасархай шугамын дагуу хар хүрээтэй гулсдаг шилэн хаалга (2 хавтас, ≈ 240×210 см) хийвэл хоол хийх үнэр, чийг угаалгын хэсэгт орохгүй, гэрэл орсоор байна.

## Өрөө тус бүрийн тавилга, хэмжээ, материал

### 03 Зочны / хоолны өрөө

3.2 × 4.6 м

| Тавилга | Ө × Г × Ө, см | Материал / өнгө |
|---|---|---|
| Буйдан, 3 хүний | 210×90×80 | Маалинган бүрээс #CFC6B8, салдаг бүрээстэй |
| Кофе ширээ | 100×60×40 | Цайвар царс, доод тавиуртай |
| ТВ тавиур | 180×40×45 | Царсны шпон, хар бариулгүй |
| ТВ | 50–55" | Үзэх зай ~1.9 м; төв нь 105 см |
| Хоолны ширээ | 120×80×75 | Царс; 4 сандал 45×50×80 |
| Унжлагат гэрэл | Ø45 | Ширээнээс 80 см дээр, 2700K |
| Хивс | 170×240 | Цайвар элсэн #E6DCCB |
| Гэрэл | 6 + 1 | Downlight 3000K ×6 + шалны гэрэл |

Буйдан баруун хананд (цонхны эсрэг биш), ТВ зүүн хананд sage онцлох ханатай. Таазанд L-хайрцаг + далд LED (сонголт).

### 01 Мастер унтлагын өрөө

3.2 × 3.9 м

| Тавилга | Ө × Г × Ө, см | Материал / өнгө |
|---|---|---|
| Ор, Queen (хүрээ) | 160×205×110 | Матрас 152×190; даавуун толгой, хадгалах |
| Шөнийн ширээ ×2 | 42×40×50 | Царс |
| Хувцасны шүүгээ | 155×60×240 | Эргэдэг хаалга, матт цагаан + царс |
| Будуарын ширээ | 80×42×75 | Царс, дээр нь Ø50 дугуй толь |
| Ханын гэрэл ×2 | — | 2700K, шалнаас 120 см |
| Хөшиг | цонх +30 | Блэкаут + тюль |

Орны 2 талд 60+ см зам. Орны толгойн хана sage. King ор (190×210) багтах боловч шүүгээний урд зай 70 см болж багасна.

### 02 Унтлагын өрөө 2

3.0 × 3.1 м

| Тавилга | Ө × Г × Ө, см | Материал / өнгө |
|---|---|---|
| Ор, Super single (хүрээ) | 120×200×90 | Матрас 107×190; доор нь татдаг 2-р ор (сонголт) |
| Ажлын ширээ | 120×60×75 | Царс, кабель нуух нүхтэй |
| Ажлын сандал | 60×60×95 | Эргономик |
| Ханын тавиур | 120×25 | Ширээнээс 45 см дээр |
| Хувцасны шүүгээ | 160×55×240 | Гулсдаг хаалга, матт цагаан |
| Гэрэл | 1 + 1 | LED панел 3000K + ширээний чийдэн 4000K |

### 10 Гал тогоо / ахуйн хэсэг

2.7 × 3.4 м

| Элемент | Ө × Г × Ө, см | Материал / өнгө |
|---|---|---|
| Доод шүүгээ (шулуун) | 260×60×88 | Фанер + HPL, матт цагаан |
| Дээд шүүгээ | 260×35×70 | Sage матт; доод ирмэг 150 см |
| Тавцан | 20 мм | Кварц, цагаан |
| Угаалтуур + плита | 80×45 / 60 | Ган угаалтуур; индукц 2–3 зуух + сорогч |
| Хөргөгч | 70×70×185 | 2 хаалгатай |
| Угаалгын + хатаагч (давхарласан) | 60×65×170 | Ахуйн хэсэгт, давхарлах хүрээтэй |
| Хувцас хатаах тавиур | 120 урт | Таазанд өлгөдөг, буулгадаг |
| Шилэн хуваалт (сонголт) | ≈ 240×210 | Хар хүрээтэй гулсдаг шил |

### 07 · 08 Угаалгын өрөө ×2

| Элемент | Ө × Г × Ө, см | Материал / өнгө |
|---|---|---|
| Угаалтуурын шүүгээ | 60×45×50 | Дүүжин; мастерт царс, нийтийнд цагаан |
| Толин шүүгээ | 60×12×70 | LED, 4000K |
| Жорлон | 38×62 | Цагаан |
| Шүршүүр | 80×85 | 8 мм шилэн хаалт, урт ус зайлуулагч |
| Хавтан | 300×300 / 300×600 | Чулуун саарал; мастерт нэг хананд sage хавтан |
| Агааржуулах сэнс | — | Гэрэлтэй хамт асдаг |

### 04 · 05 · 06 Хонгил, орох хэсэг, Shelter

| Элемент | Ө × Г × Ө, см | Материал / өнгө |
|---|---|---|
| Гутлын шүүгээ | 100×35×120 | Царс + цагаан; доод талд 20 см нээлттэй |
| Суудалтай вандан (сонголт) | 80×35×45 | Гутал өмсөхөд |
| Хонгилын урлаг / зураг | 60×80 | Нүдний түвшин 150 см |
| Shelter тавиур | 90×30×180 | Чөлөөтэй зогсох; ханад бэхлэхгүй |
| Гэрэл | 4 ш | Downlight 3000K |

### Σ Тоо хэмжээ (ойролцоо)

| Материал | Тоо | Тайлбар |
|---|---|---|
| SPC шал | ~49 м² | Өрөө 1, 2, 3, 4, 5 — 10% нөөцтэй |
| Ханын будаг | ~30 л | ~150 м² хана, 2 давхар |
| Sage будаг | ~5 л | ТВ-ийн ард, мастер орны толгой |
| Downlight | ~13 ш | Зочны/хоолны 6, хонгил/орох 4, гал тогоо 3 |
| Залгуур (нэмэлт) | ~10 ш | ТВ 2, орны хажуу 4, ажлын ширээ 2, тавцан 2 |

Өрөөний хэмжээ нь HDB-ийн зургийн харьцаа ба 64 м² дотоод талбайгаас тооцсон ойролцоо утга (±10–15 см). Суурилуулсан тавилга захиалахаас өмнө газар дээр нь хэмжинэ.

ТӨЛӨВЛӨГӨӨ 04 · 4-ӨРӨӨ

# 4-өрөө орон сууц

3–5 хүнтэй гэр бүлд. Зочны ба хоолны хэсэг нэг тэнхлэгт, 3 унтлагын өрөө хонгилын дагуу. Гал тогоо тусдаа, хажууд нь угаалга, хатаалгын service yard.

Нийт талбай
**90 м²**

Дотоод талбай
**86 м²**

Өрөө
**3 унтлагын · 2 угаалгын**

Хэнд
**3–5 хүнтэй гэр бүл**

## Тавилгын байршлын зураг

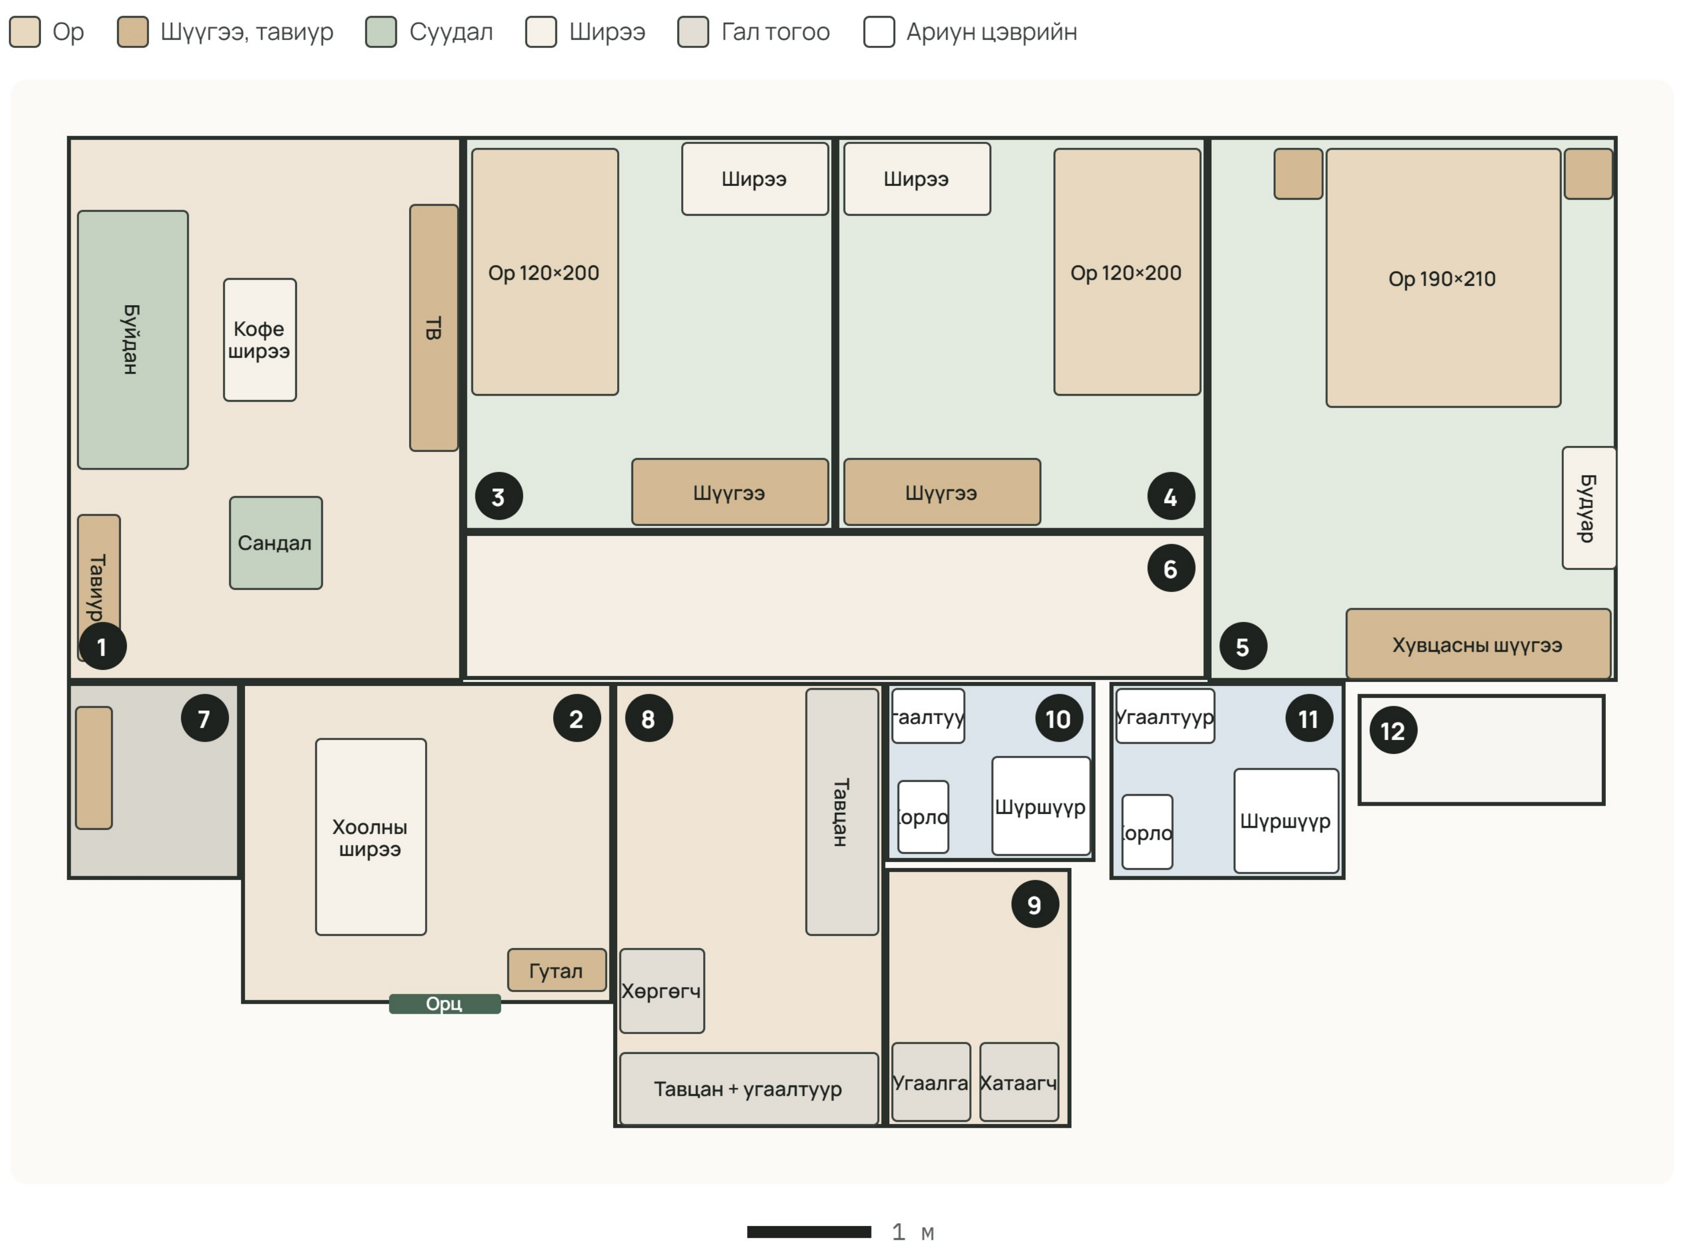

## Өрөөний хэмжээ (ойролцоо)

| № | ӨРӨӨ | ХЭМЖЭЭ, М | М² |
|---|---|---|---|
| 1 | Зочны өрөө | 3.2 × 4.4 | 14.1 |
| 2 | Хоолны хэсэг | 3.0 × 2.6 | 7.8 |
| 3 | Унтлагын өрөө 2 | 3.0 × 3.2 | 9.6 |
| 4 | Унтлагын өрөө 3 | 3.0 × 3.2 | 9.6 |
| 5 | Мастер унтлагын | 3.3 × 4.4 | 14.5 |
| 6 | Хонгил | 6.0 × 1.2 | 7.2 |
| 7 | Shelter | 1.4 × 1.6 | 2.2 |
| 8 | Гал тогоо | 2.2 × 3.6 | 7.9 |
| 9 | Service yard | 1.5 × 2.1 | 3.2 |
| 10 | Нийтийн угаалгын | 1.7 × 1.45 | 2.5 |
| 11 | Мастер угаалгын | 1.9 × 1.6 | 3.0 |
| 12 | Агааржуулагчийн тавиур | 2.0 × 0.9 | 1.8 |

## Өрөө тус бүрийн тавилга, хэмжээ, материал

### 01 Зочны өрөө

3.2 × 4.4 м

| ТАВИЛГА | Ө × Г × Ө, СМ | МАТЕРИАЛ / ӨНГӨ |
|---|---|---|
| Буйдан, 3 хүний | 210×90×80 | Маалинган бүрээс #CFC6B8 |
| Нэг хүний сандал | 75×75×80 | Царсан хүрээ, sage даавуу |
| Кофе ширээ | 100×60×40 | Цайвар царс |
| ТВ тавиур | 200×40×45 | Царсны шпон; ард нь sage хана |
| ТВ | 55" | Үзэх зай ~1.9 м; төв 105 см |
| Номын тавиур | 120×35×180 | Царс + хар металл |
| Хивс | 200×250 | Цайвар элсэн #E6DCCB |
| Гэрэл | 6 + 1 | Downlight 3000K ×6 + шалны гэрэл; L-хайрцаг LED |

### 02 · 07 Хоолны хэсэг, орц, Shelter

3.0 × 2.6 м

| ТАВИЛГА | Ө × Г × Ө, СМ | МАТЕРИАЛ / ӨНГӨ |
|---|---|---|
| Хоолны ширээ, 6 хүний | 160×90×75 | Царс, бөөрөнхий ирмэг |
| Сандал ×6 | 45×50×80 | Царс + маалинган суудал |
| Унжлагат гэрэл (шугаман) | 120 урт | Хар матт, 2700K, ширээнээс 80 см |
| Гутлын шүүгээ | 80×35×120 | Царс + цагаан, орцны хажууд |
| Толь | 50×170 | Хар нарийн хүрээ |
| Shelter тавиур | 100×30×180 | Чөлөөтэй зогсох; ханад бэхлэхгүй |

### 05 Мастер унтлагын өрөө

3.3 × 4.4 м

| ТАВИЛГА | Ө × Г × Ө, СМ | МАТЕРИАЛ / ӨНГӨ |
|---|---|---|
| Ор, King (хүрээ) | 190×210×110 | Матрас 183×190; даавуун толгой |
| Шөнийн ширээ ×2 | 40×42×50 | Царс |
| Хувцасны шүүгээ | 215×60×240 | Гулсдаг, матт цагаан + царс, дотроо LED |
| Будуарын ширээ | 100×45×75 | Царс; дээр нь 60×80 толь |
| Ханын гэрэл ×2 | – | 2700K, шалнаас 120 см |
| Хөшиг | цонх +30 | Блэкаут + тюль |

Орны толгойн хана sage, хажуу тал бүрт 60 см зам; шүүгээний урд 1.6 м чөлөөтэй.

### 03 · 04 Унтлагын өрөө 2 ба 3

3.0 × 3.2 м

| ТАВИЛГА | Ө × Г × Ө, СМ | МАТЕРИАЛ / ӨНГӨ |
|---|---|---|
| Ор, Super single (хүрээ) | 120×200×90 | Матрас 107×190; доор нь татдаг ор (сонголт) |
| Ажлын ширээ | 120×60×75 | Царс |
| Ажлын сандал | 60×60×95 | Эргономик |
| Ханын тавиур ×2 | 120×25 | Ширээнээс 45 ба 85 см дээр |
| Хувцасны шүүгээ | 160×55×240 | Гулсдаг хаалга, матт цагаан |
| Гэрэл | 1 + 1 | LED панел 3000K + ширээний 4000K |

Хоёр өрөө толин тусгал байрлалтай. Хүүхдийн өрөөнд онцлох хана цайвар элсэн эсвэл sage.

### 08 · 09 Гал тогоо ба service yard

2.2 × 3.6 м

| ЭЛЕМЕНТ | Ө × Г × Ө, СМ | МАТЕРИАЛ / ӨНГӨ |
|---|---|---|
| Доод шүүгээ, L хэлбэр | 200 + 210 × 60 × 88 | Фанер + HPL, матт цагаан |
| Дээд шүүгээ | 200 + 150 × 35 × 70 | Sage матт; доод ирмэг 150 см |
| Тавцан | 20 мм | Кварц, цагаан |
| Угаалтуур + плита | 80×45 / 60–70 | Ган угаалтуур; индукц 3 зуух + сорогч |
| Хөргөгч | 70×70×185 | Зүүн хананд |
| Угаалгын + хатаагч машин | 2 × 60×60×85 | Service yard-д зэрэгцээ, дээр нь 140×60 тавцан |
| Хатаах тавиур | 120 урт | Таазанд өлгөдөг |
| Шүүр, хадгалах шүүгээ | 60×40×200 | Service yard, цагаан |

### 10 · 11 Угаалгын өрөө ×2

| ЭЛЕМЕНТ | Ө × Г × Ө, СМ | МАТЕРИАЛ / ӨНГӨ |
|---|---|---|
| Угаалтуурын шүүгээ | 80 / 60 ×45×50 | Мастерт 80 см царс, нийтийнд 60 см цагаан |
| Толин шүүгээ | 80 / 60 ×12×70 | LED, 4000K |
| Жорлон | 38×62 | Цагаан |
| Шүршүүр | 85×85 / 80×80 | 8 мм шилэн хаалт |
| Хавтан | 300×300 / 300×600 | Чулуун саарал; мастерт нэг хана sage |
| Агааржуулах сэнс | – | Гэрэлтэй хамт |

## Σ Тоо хэмжээ (ойролцоо)

| МАТЕРИАЛ | ТОО | ТАЙЛБАР |
|---|---|---|
| SPC шал | ~69 м² | Өрөө 1–6 — 10% нөөцтэй |
| Ханын будаг | ~38 л | ~190 м² хана, 2 давхар |
| Sage будаг | ~6 л | ТВ-ийн ард, мастер орны толгой, хүүхдийн өрөө |
| Downlight | ~18 ш | Зочны 6, хоолны 2, хонгил 5, гал тогоо 3, service yard 2 |
| Залгуур (нэмэлт) | ~14 ш | ТВ 2, ор бүрийн хажуу 4, ажлын ширээ 4, тавцан 3, service yard 1 |

---

Өрөөний хэмжээ нь HDB-ийн зургийн харьцаа ба 86 м² дотоод талбайгаас тооцсон ойролцоо утга (±10–15 см). Суурилуулсан тавилга захиалахаас өмнө газар дээр нь хэмжинэ.